


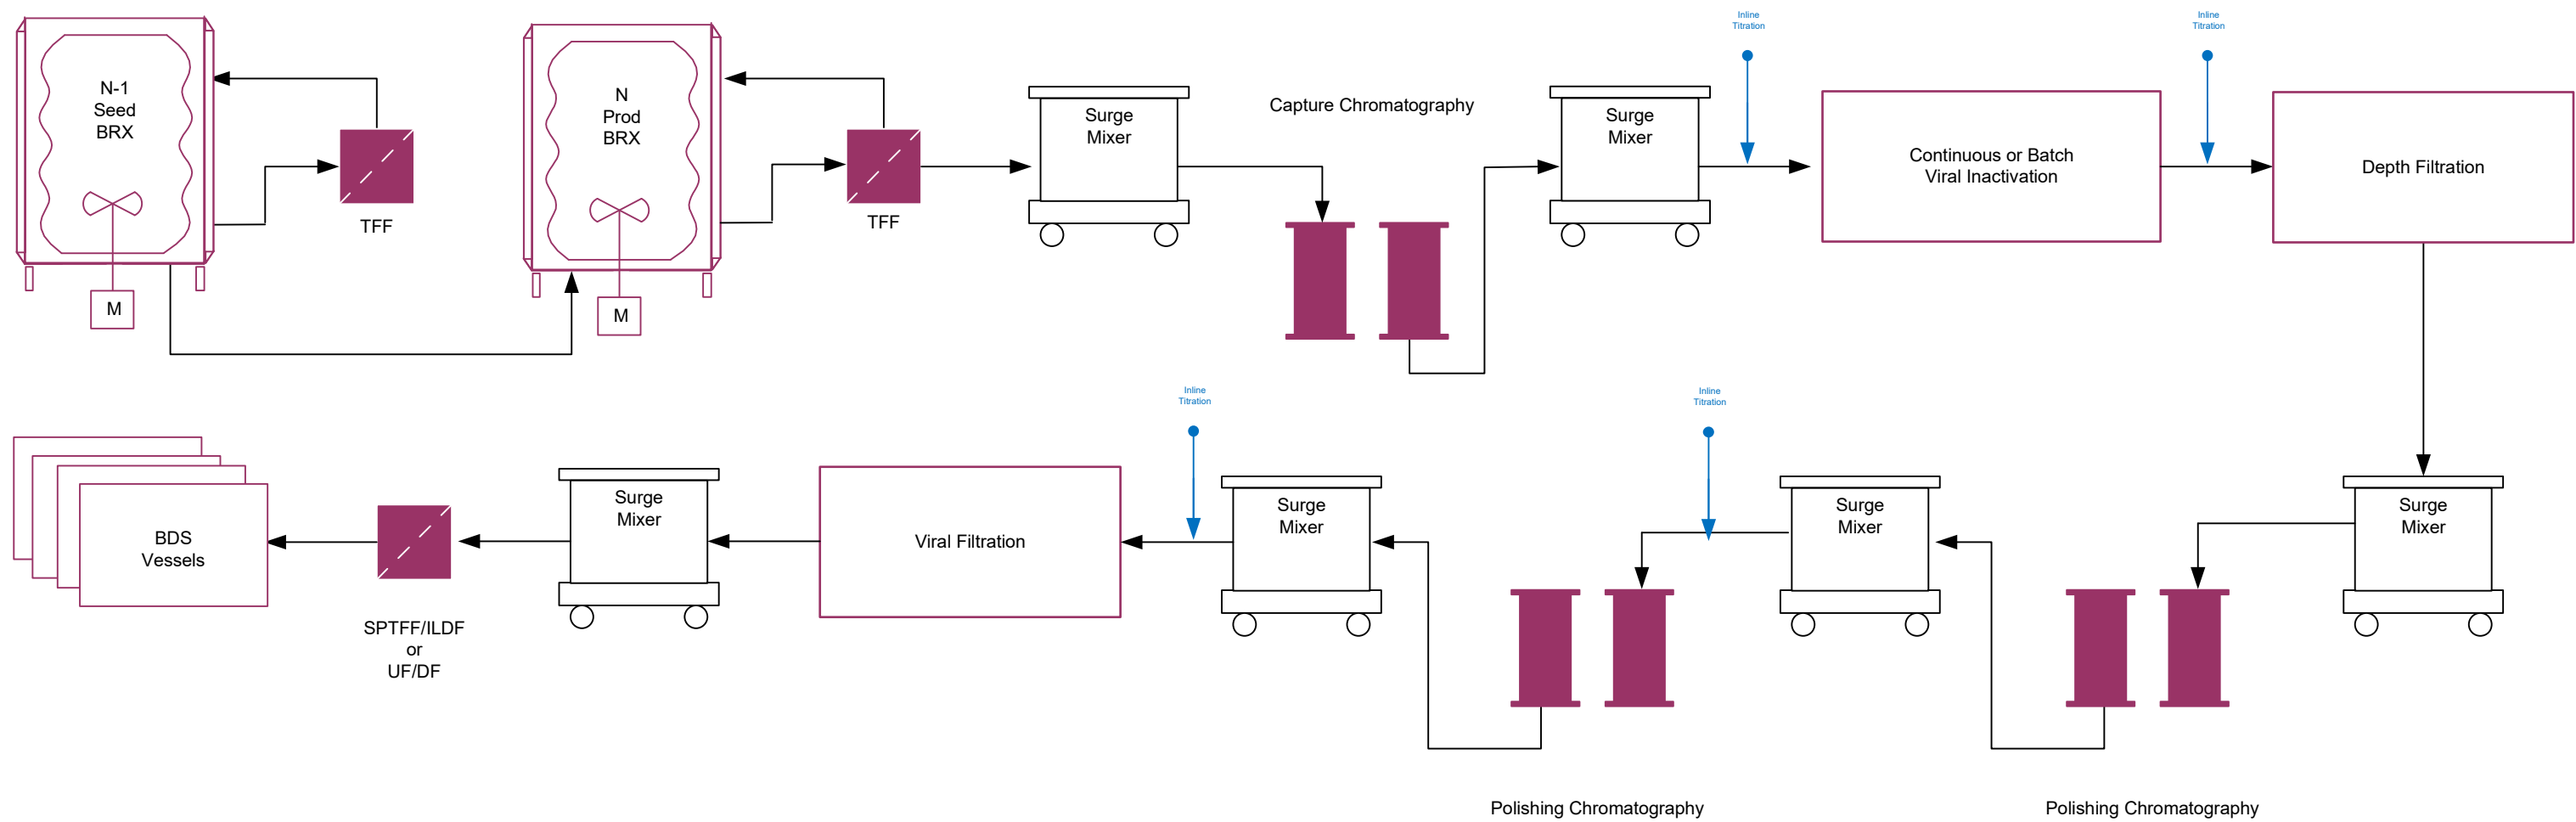

Dwg No. ICB-BFD-001  
Rev. A  
Date: 15 Oct 2020  
Wood Project No. 212XXX  
© Copyright 2020 Wood TCS